


General arrangement

Every dimension on this sheet is invented.

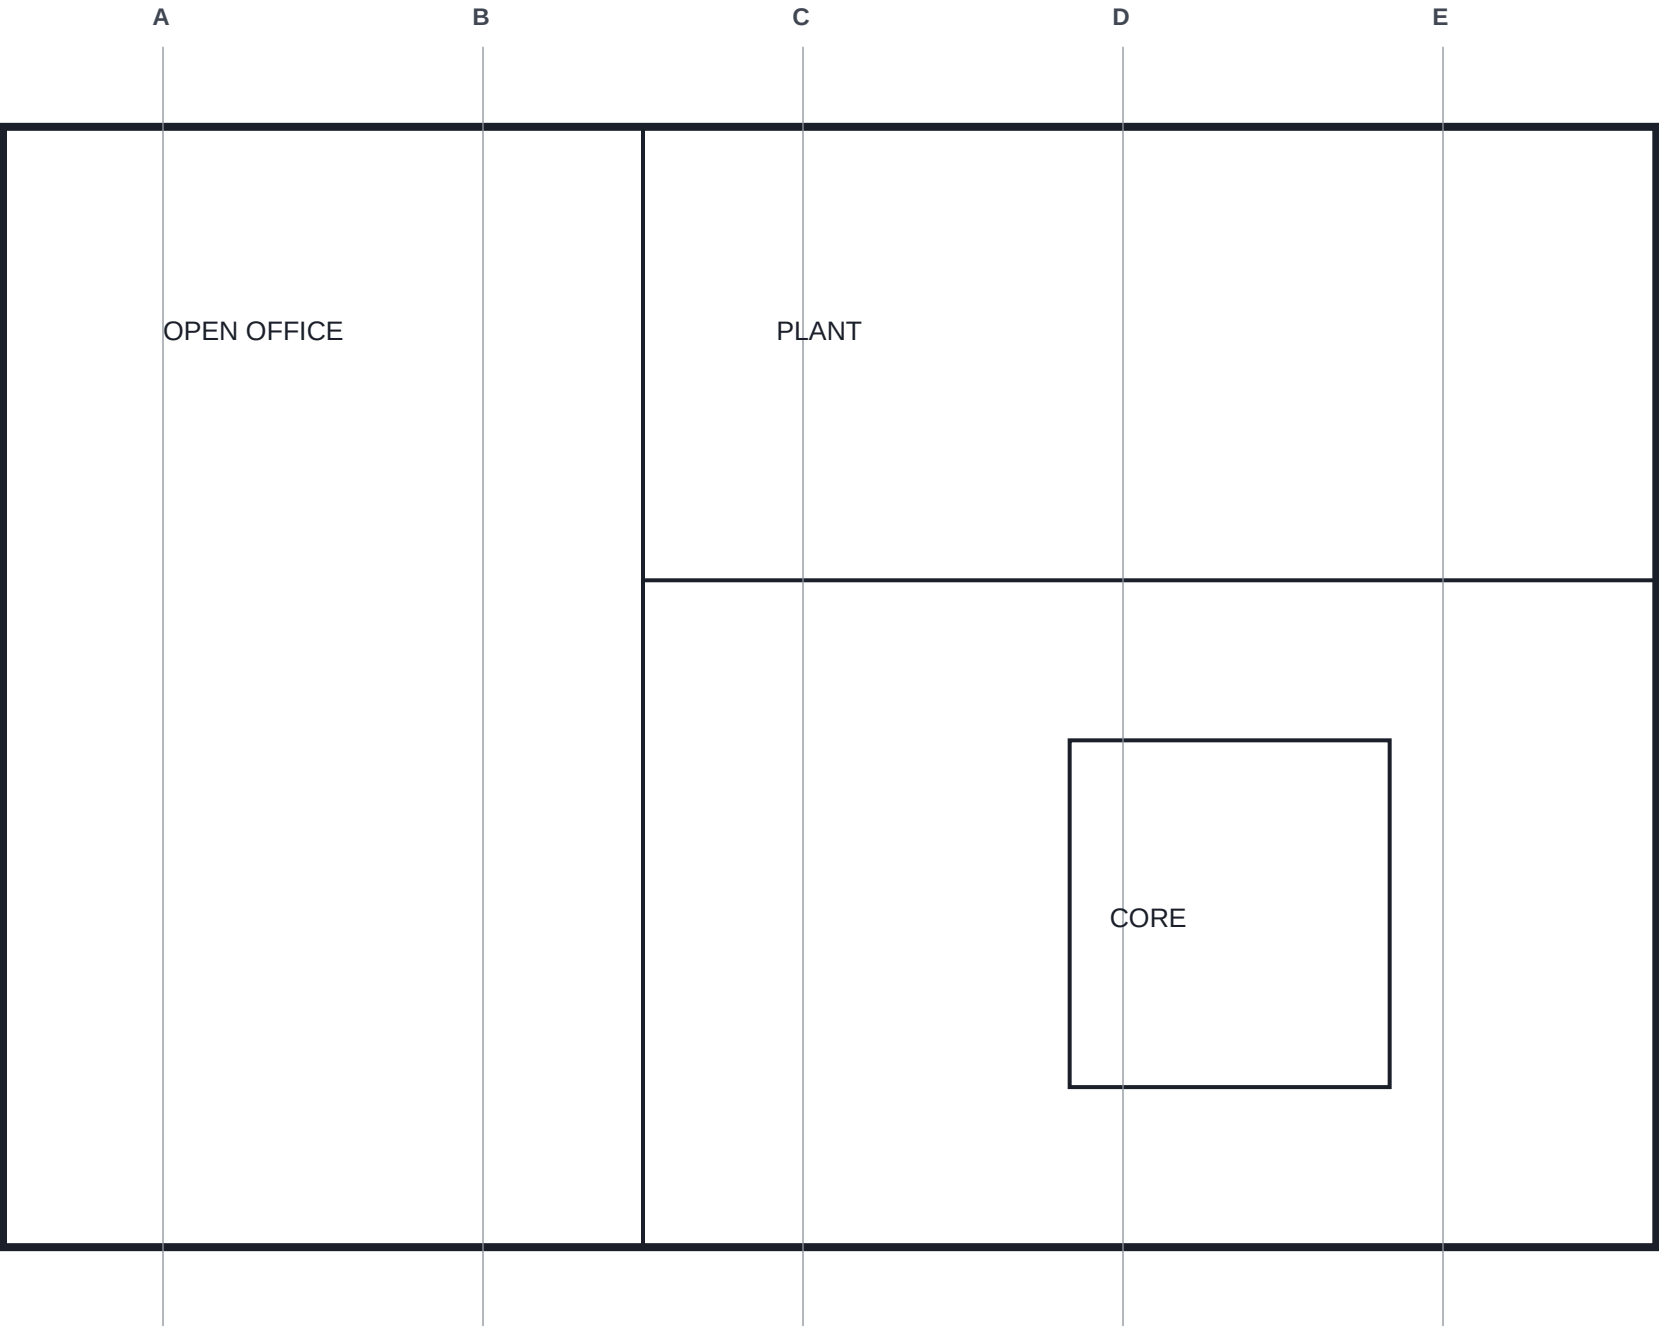

SAMPLE PROJECT


Synthetic content for demonstration
No real asset, party or location

GENERAL ARRANGEMENT — LEVEL 02

Sheet 1 of 3 Rev P01 Not for construction

Section A–A

Storey heights are illustrative only.

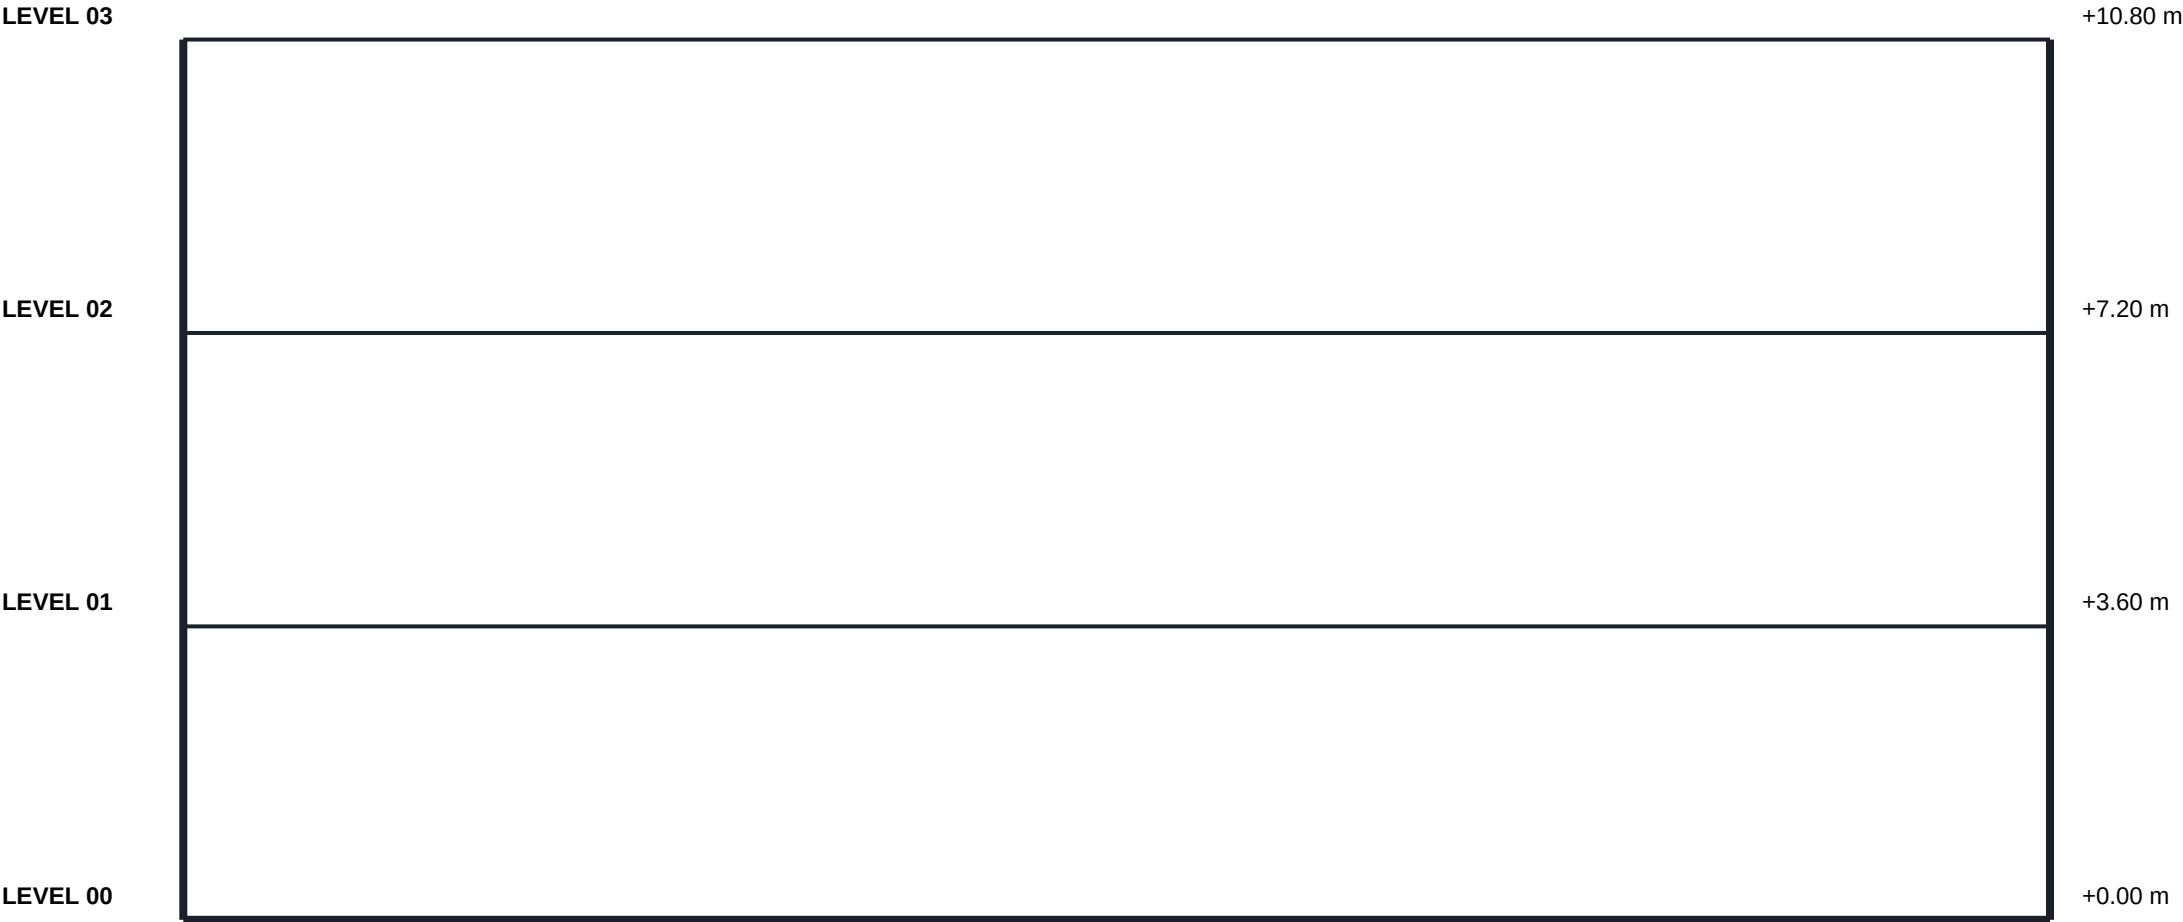

SAMPLE PROJECT

Synthetic content for demonstration
No real asset, party or location

SECTION A–A

Sheet 2 of 3 Rev P01 Not for construction

General notes

This document is synthetic sample content generated for the embed demo.
It describes no real building, no real party, and no real location.

The viewer is given this file by URL. It fetches it once, renders it, and
holds any markup you draw until the host takes it. Nothing is stored here.

Search for the word FERROUS to see the text layer and the search index at
work: it appears twice, both times on this sheet and nowhere else in the
document, so a search should take you here and report two hits.

FERROUS fixings are indicated on the general arrangement as filled squares.

Markup you draw is emitted to the host as viewer.markupCreated. The demo
host stores it against this document and hands it back on reload, which is
the whole persistence story: the viewer forgets, the host remembers.

SAMPLE PROJECT

Synthetic content for demonstration
No real asset, party or location

GENERAL NOTES

Sheet 3 of 3 Rev P01 Not for construction